SUPPLY SCOPE (distributor quantities, no material prices): Nudura ICF for the basement extension below the lower-ground floor level, stock forms + 5 % waste - the 450 wall as a 457 core (unassembled XR35 panels on insert webs + 4-way connectors) and the 200 Standard walls with the internal corbel top course. From Ethos' sketch (7.7 x 18 m, 7 courses); position against the existing basement and the official drawing to follow. Raft by others.

QUOTATION - NOT FOR CONSTRUCTION

N

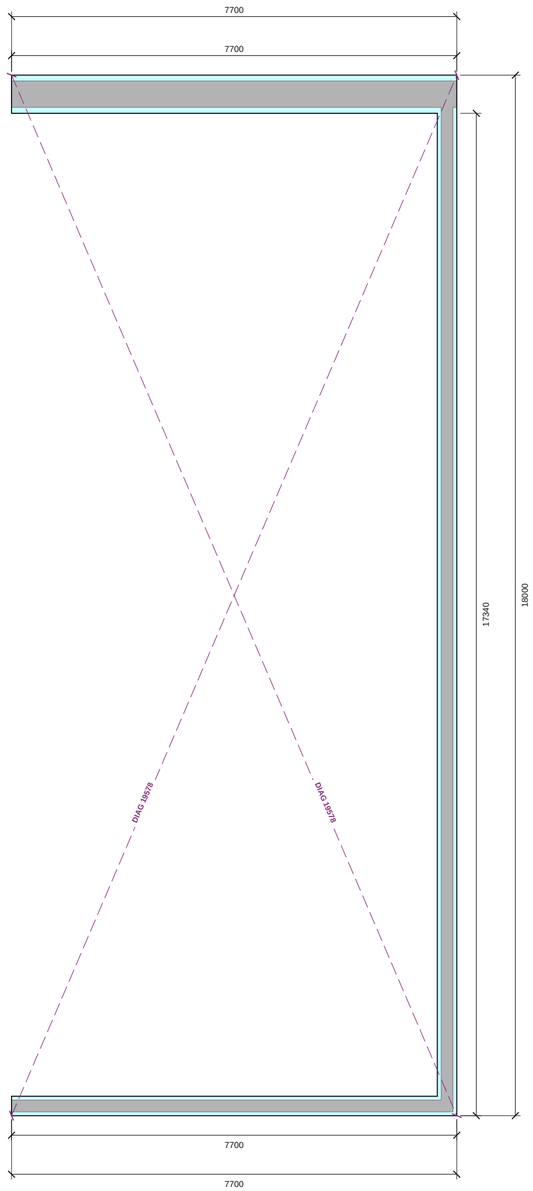

EPS insulation (Nudura form)
Concrete core
End cap at opening
Engineer's pier bars (n-H12 vertical bars in ICF pier) / WS wall starters
Setting-out check diagonal (external ICF corners)

BASEMENT EXTENSION ICF PLAN

Scale 1:75 @ A2 | Plan cut at +1480

0 1 2 3 4m

BASEMENT EXTENSION ICF SCHEDULES

OPENING SCHEDULE

Ref	Width	Height	Sill	Head	Lintel
none					

Structural openings in the ICF; sill and head above GF FFL.

NOTES

1. ICF: Nudura 8" Std, 66.7 EPS + 203.2 core + 66.7 EPS = 336.6; 9.18in XR35 Panel Series, 101.6 EPS + 457.2 core + 101.6 EPS = 660.4. Dimensions to the ICF faces.
2. Levels above GF FFL. Sill / head = structural opening in the ICF.
3. No structural drawing issued for the extension (sketch only). 450 wall as a 457 core of unassembled XR35 panels on 12in + 6in insert webs; reinforcement, the tie to the existing basement and the raft for the engineer.
4. Lintel (L-n) and steel (B-n, C-1) marks from rev -, which takes precedence.
5. Masonry walls shown for context.
6. Datum: 0 = top of the extension raft (assumed at the existing basement raft SSL-2 +40.357 - confirm).
7. From Ethos' extension sketch (7.7 x 18 m, 7 courses); the official drawing to follow.

REVISIONS

REV	DATE	DESCRIPTION
-	02.11.26	Quotation issue

Nudura™ BuildEase

CLIENT	PROJECT
Ethos Property Developments (Nudura distributor) - Mark Whalley	Basement extension, Badgers Hollow, Alderley Edge

DRAWING TITLE

BASEMENT EXTENSION ICF GENERAL ARRANGEMENT

ICF walls, openings, lintels, steel over and engineer's notes

SCALE	SIZE	DATE
1:75	A2	02.11.26
DRAWN	CHECKED	APPROVED
TS		

STATUS	DRAWING No.	REV
QUOTATION	ES26-088-GA-01	-

Do not scale. All dimensions in millimetres, levels in metres from GF FFL. Check all dimensions on site.